


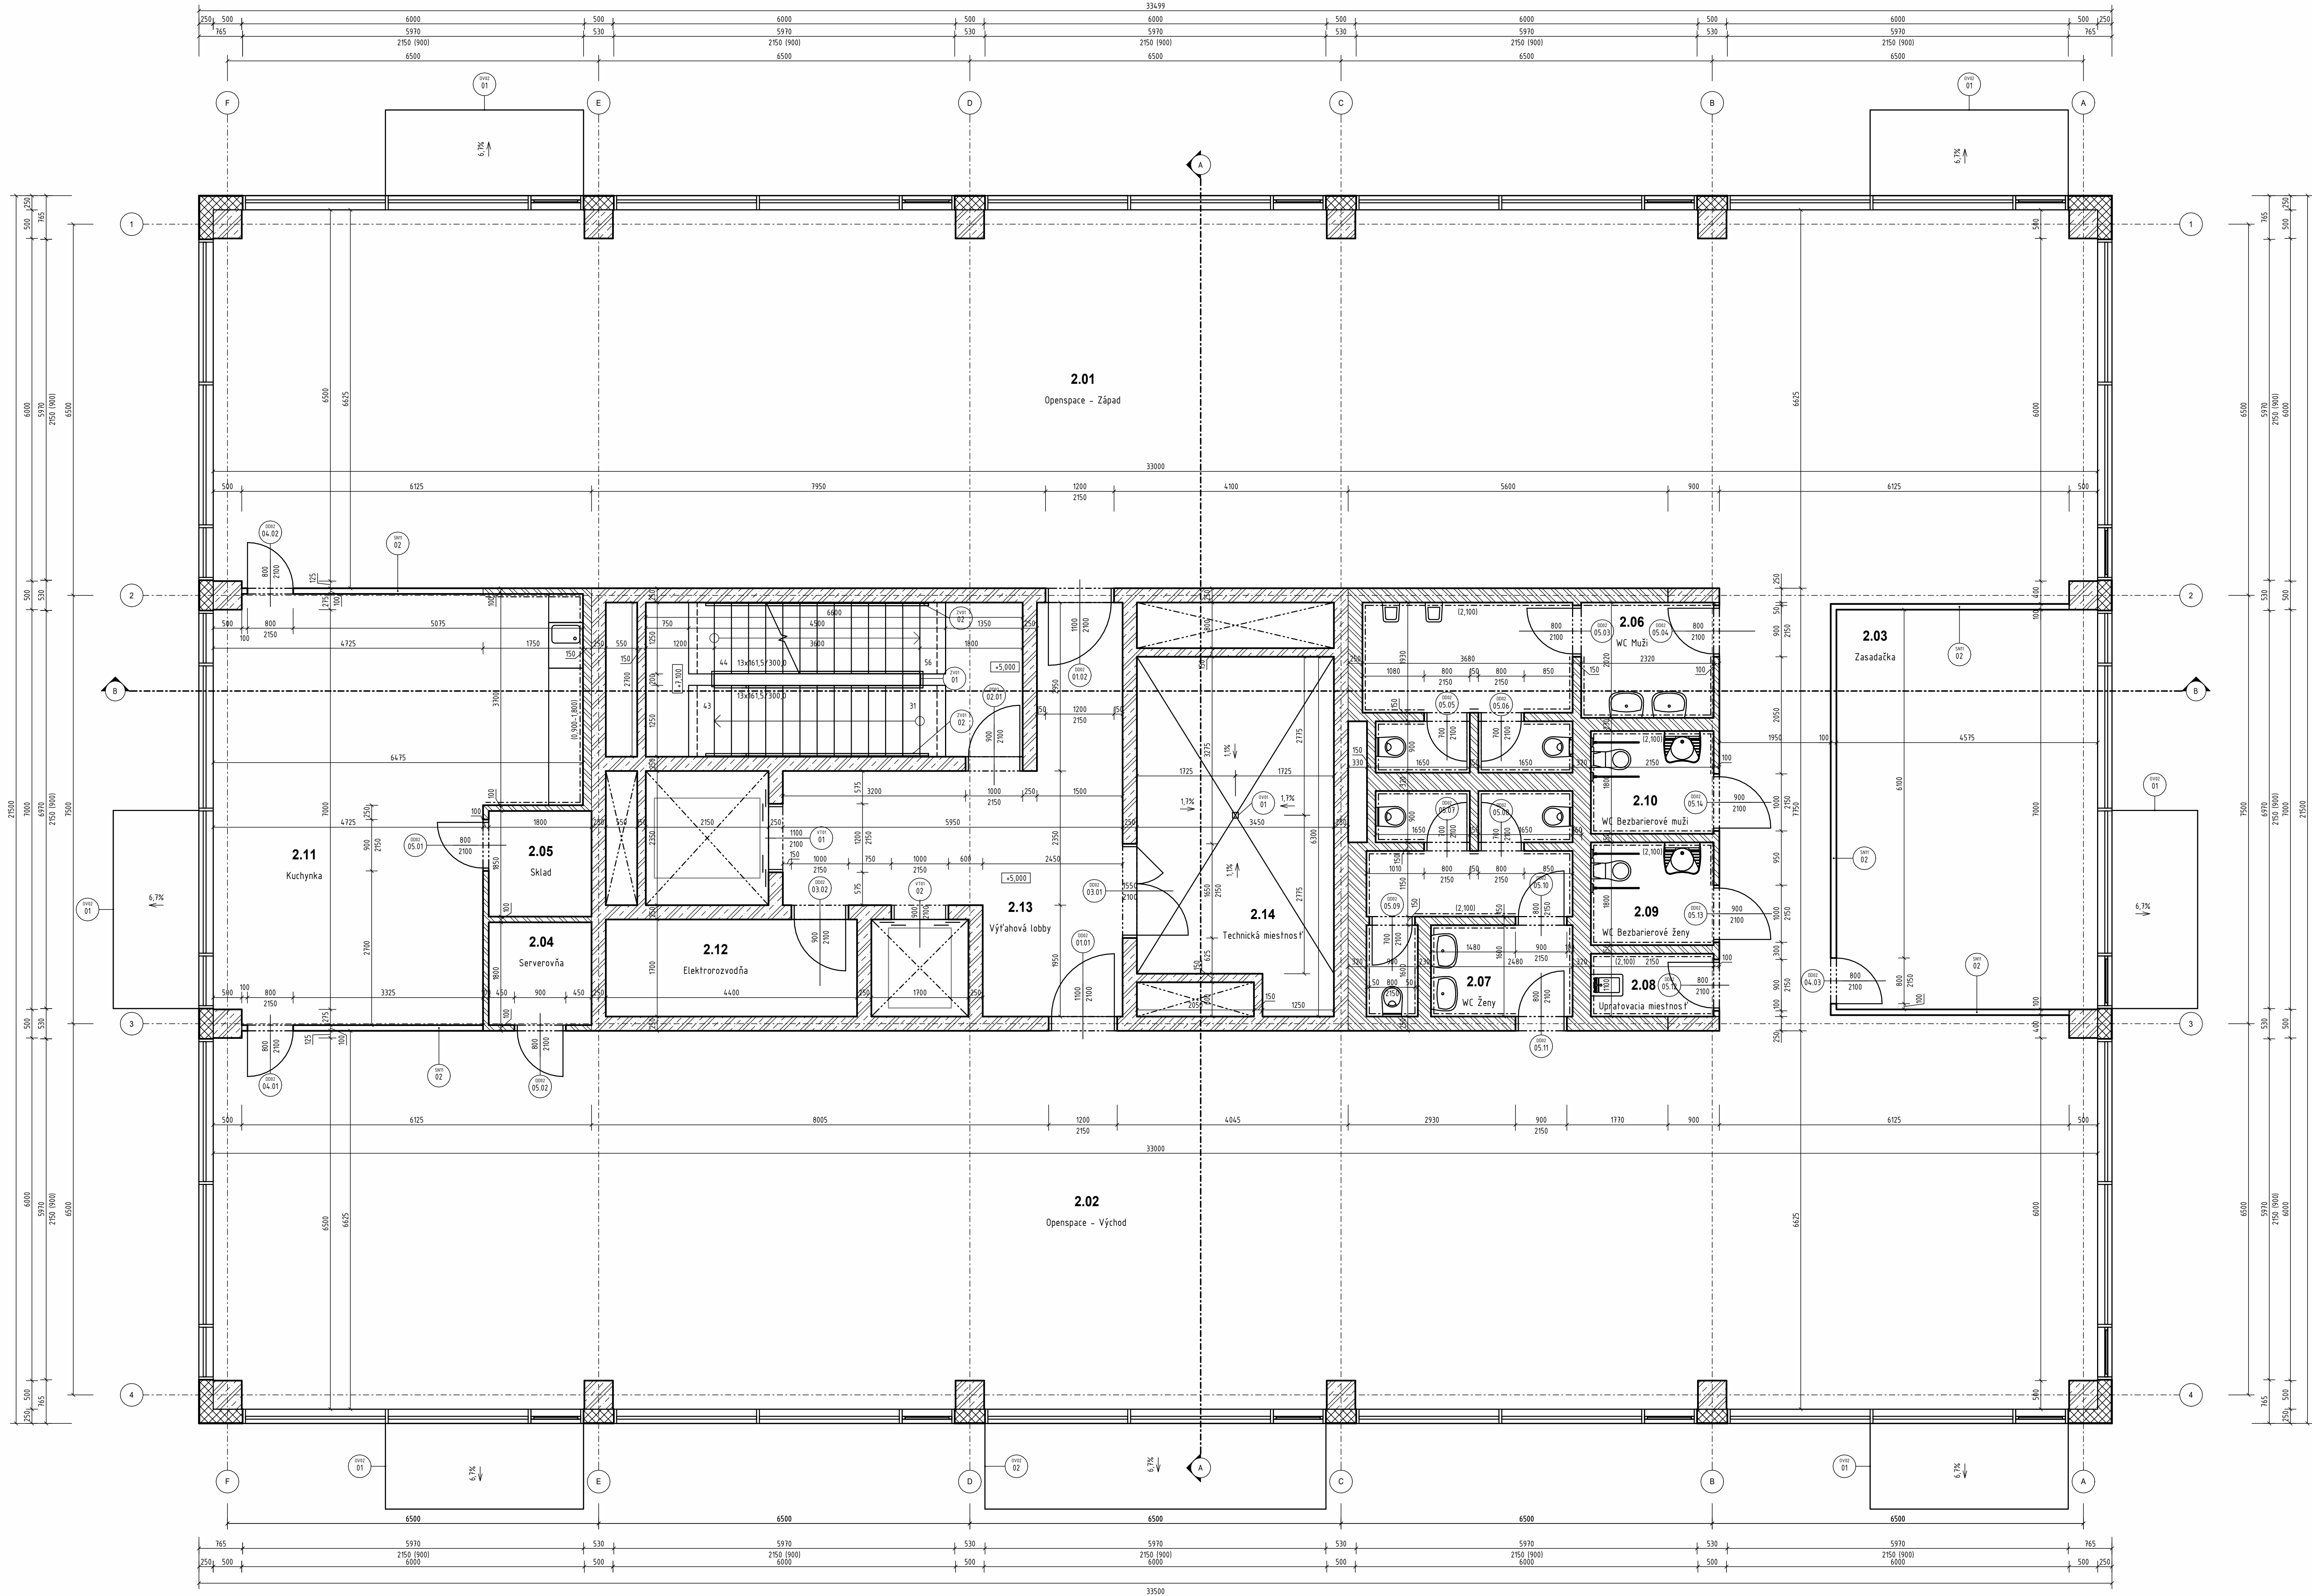

LEGENDA MIESTNOSTÍ

Číslo	Názov	Príslušnosť priestoru	Plocha [m ²]	Svetl. výška [mm]	Podlaha	Strop/Podhlad	Steny
2.01	Openpace - Západ	Nájomný priestor	230,95	3050	PD03.30 - Slučkový zářazový koberec	PH01.10 - Kazeťový SDK podhlad - štandard	Náher
2.02	Openpace - Východ	Nájomný priestor	230,95	3050	PD03.30 - Slučkový zářazový koberec	PH01.10 - Kazeťový SDK podhlad - štandard	Náher
2.03	Zasedačka	Nájomný priestor	32,90	3050	PD03.31 - Drevená podlaha	PH01.10 - Kazeťový SDK podhlad - štandard	Bez úpravy
2.04	Serverovňa	Nájomný priestor	3,24	2600	PD03.60 - Slučkový zářazový koberec	PH01.10 - Kazeťový SDK podhlad - štandard	Náher
2.05	Sklad	Nájomný priestor	3,33	2600	PD03.60 - Slučkový zářazový koberec	PH01.10 - Kazeťový SDK podhlad - štandard	Náher
2.06	WC Muži	Nájomný priestor	15,73	2600	PD02.31 - Štvorcová keramická dlažba	PH01.20 - Kazeťový SDK podhlad - do vlhka	Keramický obklad, náher
2.07	WC Ženy	Nájomný priestor	14,10	2600	PD02.31 - Štvorcová keramická dlažba	PH01.20 - Kazeťový SDK podhlad - do vlhka	Keramický obklad, náher
2.08	Upratovacia miestnosť	Nájomný priestor	2,37	2600	PD02.31 - Štvorcová keramická dlažba	PH01.20 - Kazeťový SDK podhlad - do vlhka	Keramický obklad, náher
2.09	WC Bezbarierové ženy	Nájomný priestor	3,87	2600	PD02.31 - Štvorcová keramická dlažba	PH01.20 - Kazeťový SDK podhlad - do vlhka	Keramický obklad, náher
2.10	WC Bezbarierové muži	Nájomný priestor	3,87	2600	PD02.31 - Štvorcová keramická dlažba	PH01.20 - Kazeťový SDK podhlad - do vlhka	Keramický obklad, náher
2.11	Kuchynka	Nájomný priestor	42,75	3050	PD03.10 - Slučkový zářazový koberec	PH01.10 - Kazeťový SDK podhlad - štandard	Keramický obklad, náher
2.12	Elektrozvodiňa	Technické priestory	7,48	3800	PD02.52 - Fanonopustný náteryový systém	Bez úpravy	Bez úpravy
2.13	Výťahová lobby	Spoločné priestory	23,19	3050	PD02.43 - Štvorcová keramická dlažba	PH01.10 - Kazeťový SDK podhlad - štandard	Náher
2.14	Technická miestnosť	Technické priestory	20,09	3800	PD02.52 - Fanonopustný náteryový systém	Bez úpravy	Bez úpravy

LEGENDA MATERIÁLOV

- ŽELEZOBETÓN
- PREFABRIKOVANÝ ŽELEZOBETÓN - SCHODISKOVÉ RAMENÁ
- PODKLAJNÝ BETÓN
- SAORKARTÓN
- MURIVO NENOSNÉ
- SAORKARTÓN
- LAHKÝ OBVOODOVÝ PLAŠT
- IZOLÁCIA MNERÁLNÁ
- IZOLÁCIA EPS
- IZOLÁCIA XPS
- BETÓNOVÁ DLAŽBA - EXTERIÉR
- KAČIČEK
- NÁŠYP
- ZEMINA
- HYDROIZOLÁCIA

LEGENDA ZNAČENIA

- POPSKA PRVKOV - SNM KÓD
- OV (XX) - TREDA STAVEBNÉHO PRVKU (TSP)
- 01 (XX) - PODTREDÁ STAVEBNÉHO PRVKU (PSP)
- 00 (XX) - UŽÍVATEĽSKÉ OZNAČENIE TYPU (UOT)
- 00 (XX) - IDENTIFIKÁTOR INŠTANCIE (INST)

LEGENDA PRVKOV

TSP/PSP/UOT	Popis prvku
SNM 02	Sklenené priečky, keramická, dvojité zasklenie, ref. výrobok LKOS - MERA II
ZV01 01	Schodiskové zábradlie výšky 1000 mm, osadené stĺpmi na schodiskovom ramene
ZV01 02	Schodiskové zábradlie výšky 1000 mm, osadené na ŽS stene
DV02 01	Sklenené prekrytie vstupu do budovy, 3470x1500mm, prípravené oceľovými hňami k LOP, ref. riešenie vid., výrobca LOP
DV02 02	Sklenené prekrytie vstupu do budovy, 5970x1500mm, prípravené oceľovými hňami k LOP, ref. riešenie vid., výrobca LOP
FS01 20	ETICS - Krycia omietka, penetračný náter, cementová lepiaca hmota, dosky z ľadovej vlny, suchá omietková zmes
DV01 01	Trpasť podlahová, DN10, krytá pochôdzňou mriežkou

POZNÁMKA

- Kótované v koordinátnych rozmeroch
- Súčasťou výkresovej dokumentácie je technická správa, v prípade rozporu TS a výkresovej PD, konzultovať s projektantom
- Pri vyhotovení stavby je nutné postupovať podľa platných ČSN a odsúhlasených technologických postupov
- Pri stavebných prácach musia byť dodržané platné predpisy týkajúce sa zásad a bezpečnosti ochrany zdravia pri práci
- Typ navrhnutého LOP: Schöck FWS 95-SL, U₁₀ = 0,64 W/m²K, otváracie okenné výplne sú zhotovené vo všetkých prípadoch vid. prílohy, pri osadení panelov postupovať podľa pokynov výrobcu, typové detaily a podrobný tepelotechnický výpočet vid. prílohy
- V miestnostiach s rôznymi skladbami podlahy budú osadené prechodové lišty
- Charakteristiky jednotlivých konštrukcií a prvkov v d. výpis skladieb
- Pri keramickom murive osadenie príslušného typu prekladu podľa výberu konkrétneho výrobcu
- V priestore odpadového hospodárstva na dverách alebo LOP bude osadená prefuková mriežka, súčasťou podrobného návrhu profície VZT
- Priečky a nosné steny budú ukončené spôsobom, že medzi hornou hranou priečky a stropom osadená medzera hr. 10-15 mm, ktorá bude vyplnená montážnou penou, alebo do nej bude vlietaná minerálna plst, podľa pokynov dodávateľa
- Skladby sadračkových priečiek kontrolizované v ďalšom stupni PD, s ohľadom na výsledky posúdenia stavebnej fyziky, osadené podľa typu prostredia, nutné zachovať minimálny rozmer miestnosti, ref. výrobky Knaf W15 a Knaf W13
- Prefabrikované schodiskové rameno opatříť antierkou hrúbky a typu produktu užitému na podlažiach
- Schodiskové rameno osadiť na pryzové podložky
- Nastupné a výstupné stupne schodiska kontrastne odlišť
- Výstup schodiskových podestí odlišť do systému ochrany proti kročajovému zvuku, ref. výrobky Schöck Transole
- Všetky presluby požiarne detailmi konštrukciami musia byť riadne utesnené podľa ustanovenia PBRS
- Plávajúce podlahy budú diaľované pod obvodé miestnosti
- Preslupy v základovej doske musia byť riadne utesnené proti vode a radónu
- Materiálové charakteristiky betónu a ocele budú doplnené na základe podrobných statických analýz autorizovanou osobou
- Zariadenie pomocou kódov SNM je v tomto projekte stanovené pod tabuľky hierarchie v prílohe

±0,000 = 199,1 m n.m., B.p.v., SÚRADNICOVÝ SYSTÉM JTSK

PREDMET	DIPLÓMOVÁ PRÁCA	FORMÁT	1150x594
VYPRACOVAL	ING. SAMUEL AUGUSTÍN	DÁTUM	01/2025
VEDÚCI PRÁCE	PROF. ING. MILAN OSTRÝ Ph.D.	STUPEN PD	Č. VÝKRES
STAVEBNÍK	KAROL OLDŘICH, INTERNÁTOVÁ 2, KAMENANY 821	MERÍTKO	1 : 50
MIESTO STAVBY	BRNO, č. PARCELY 966/1, KÚ. BRNO-TRNITÁ	Č. VÝKRES	D.1.102
NÁZOV STAVBY	OFFICE CENTRUM BRNO		
STAVEBNÝ OBJEKT	S0.01 POLYFUNKČNÝ OBJEKT		
ČASŤ	D.1.1 ARCHITEKTONICKO-STAVEBNÉ RIŠENIE		
OBSAH:	PÓDORYS 2NP		