

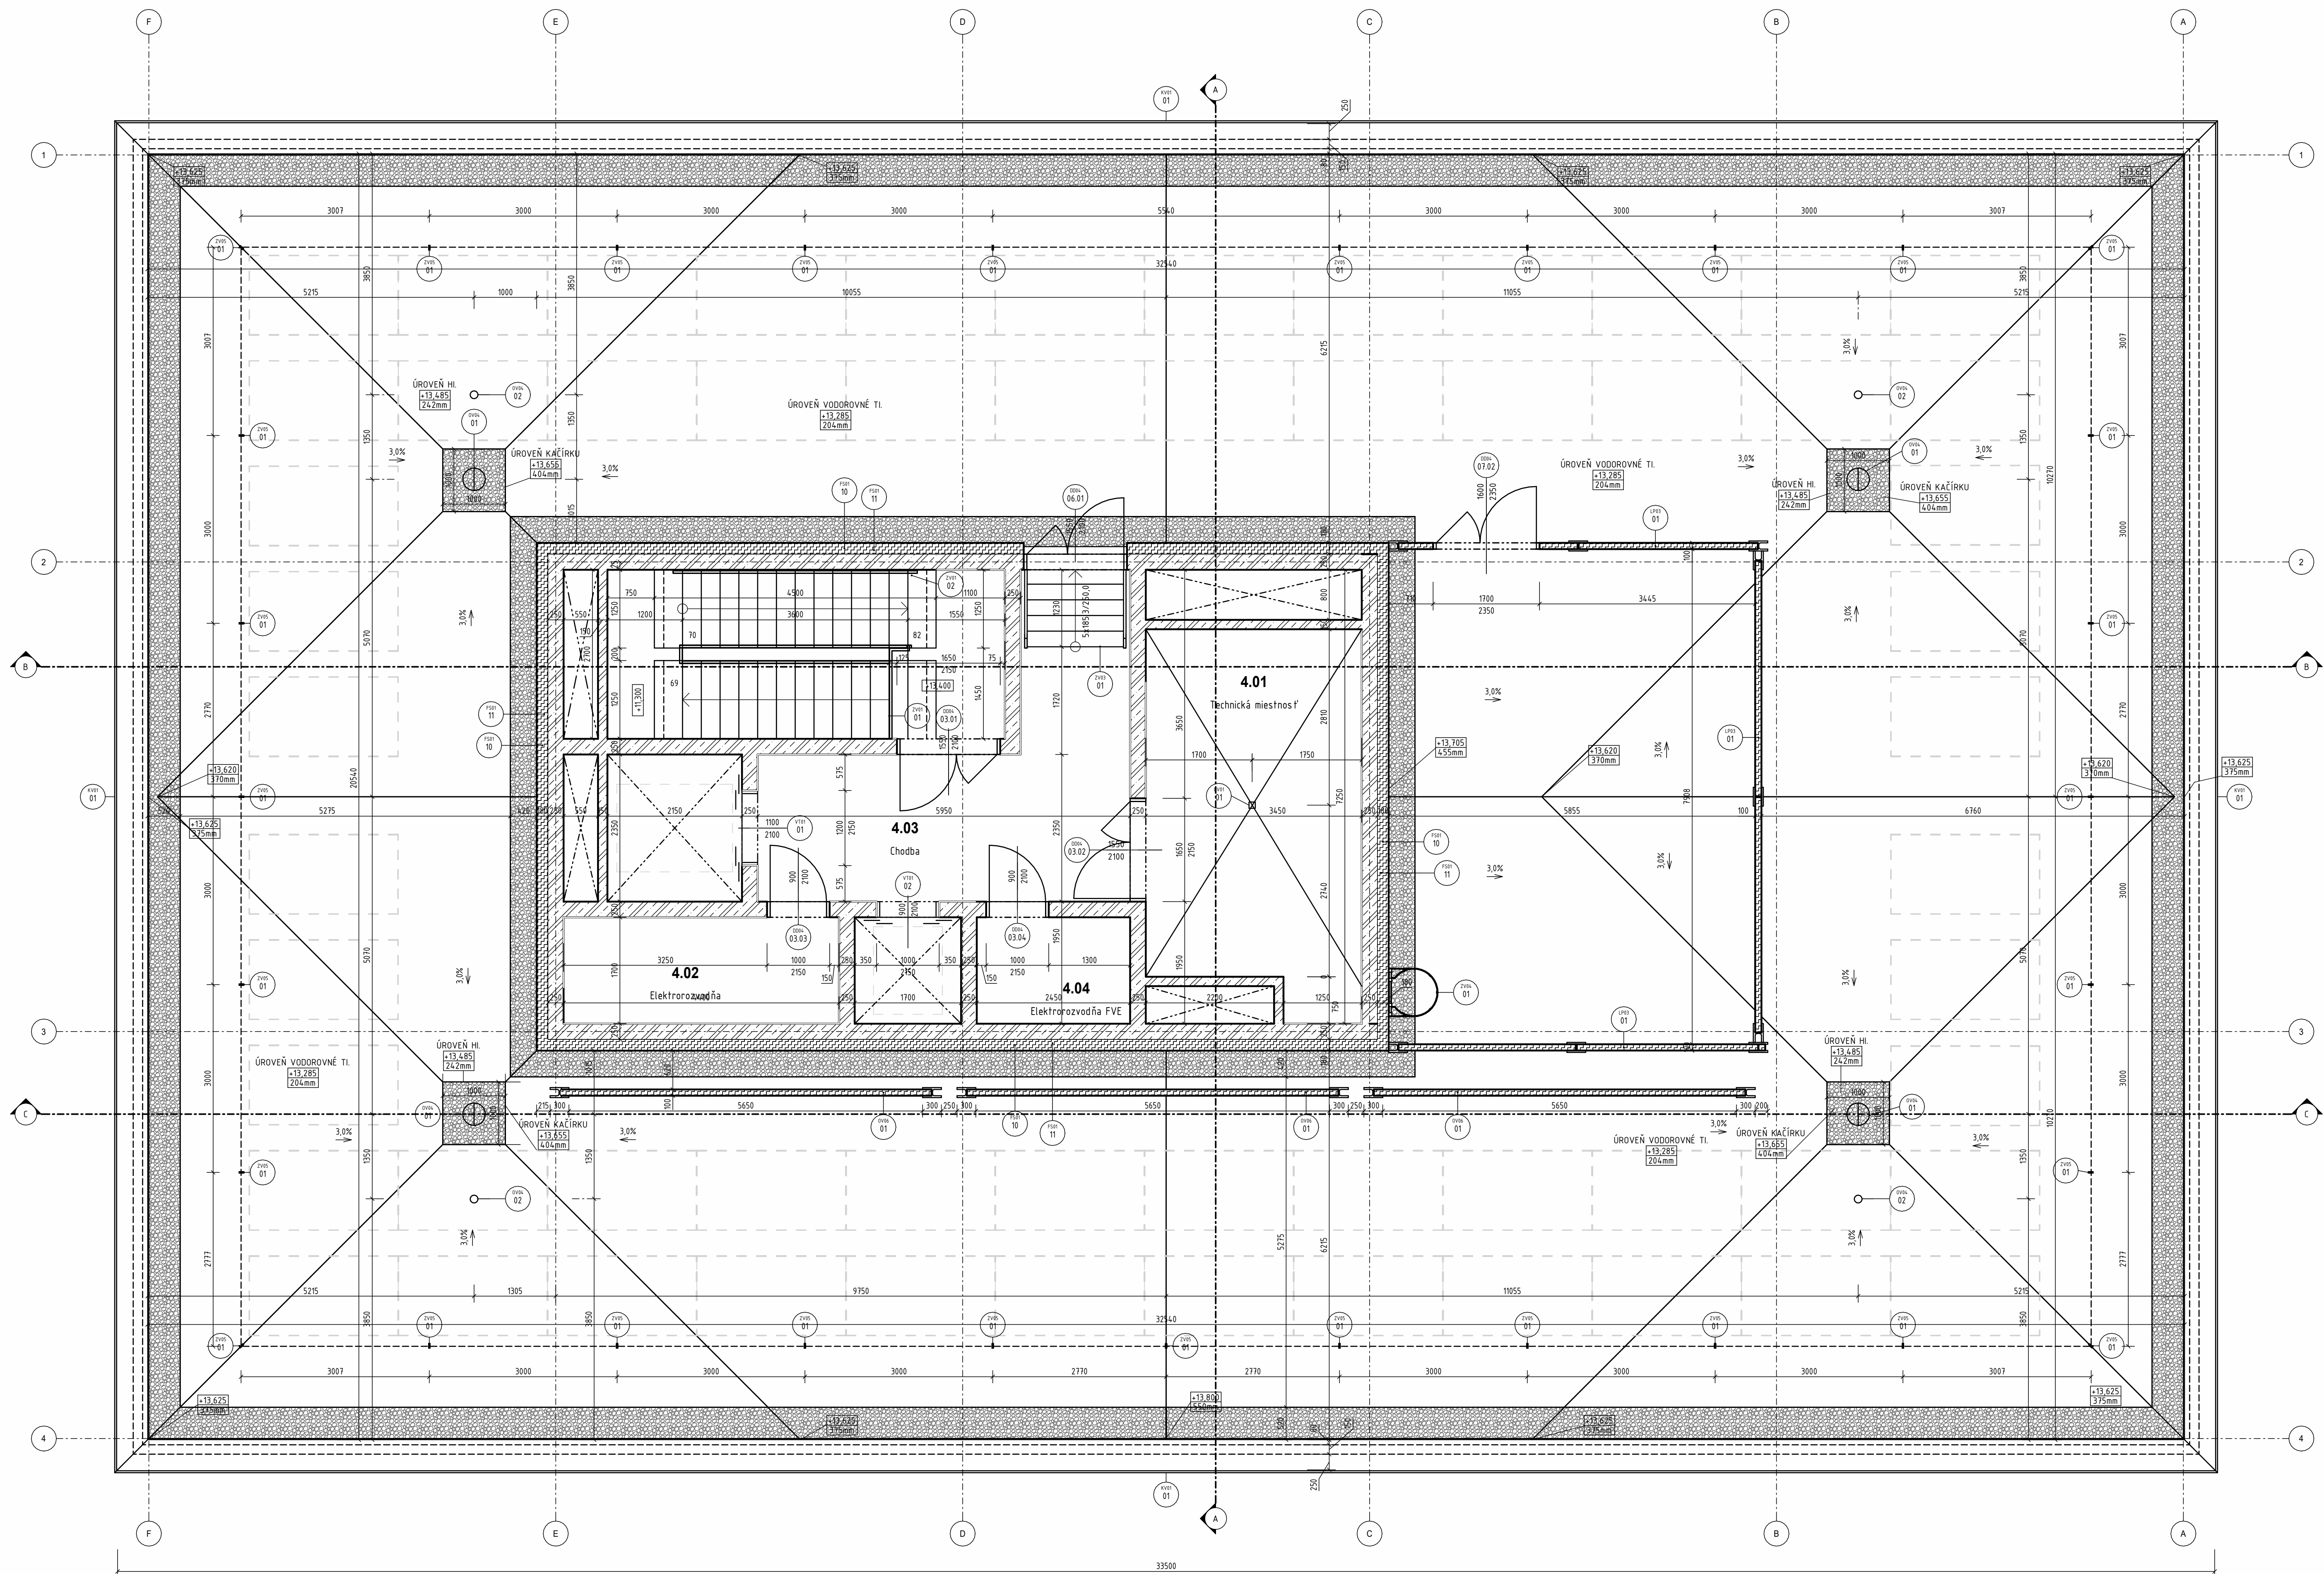


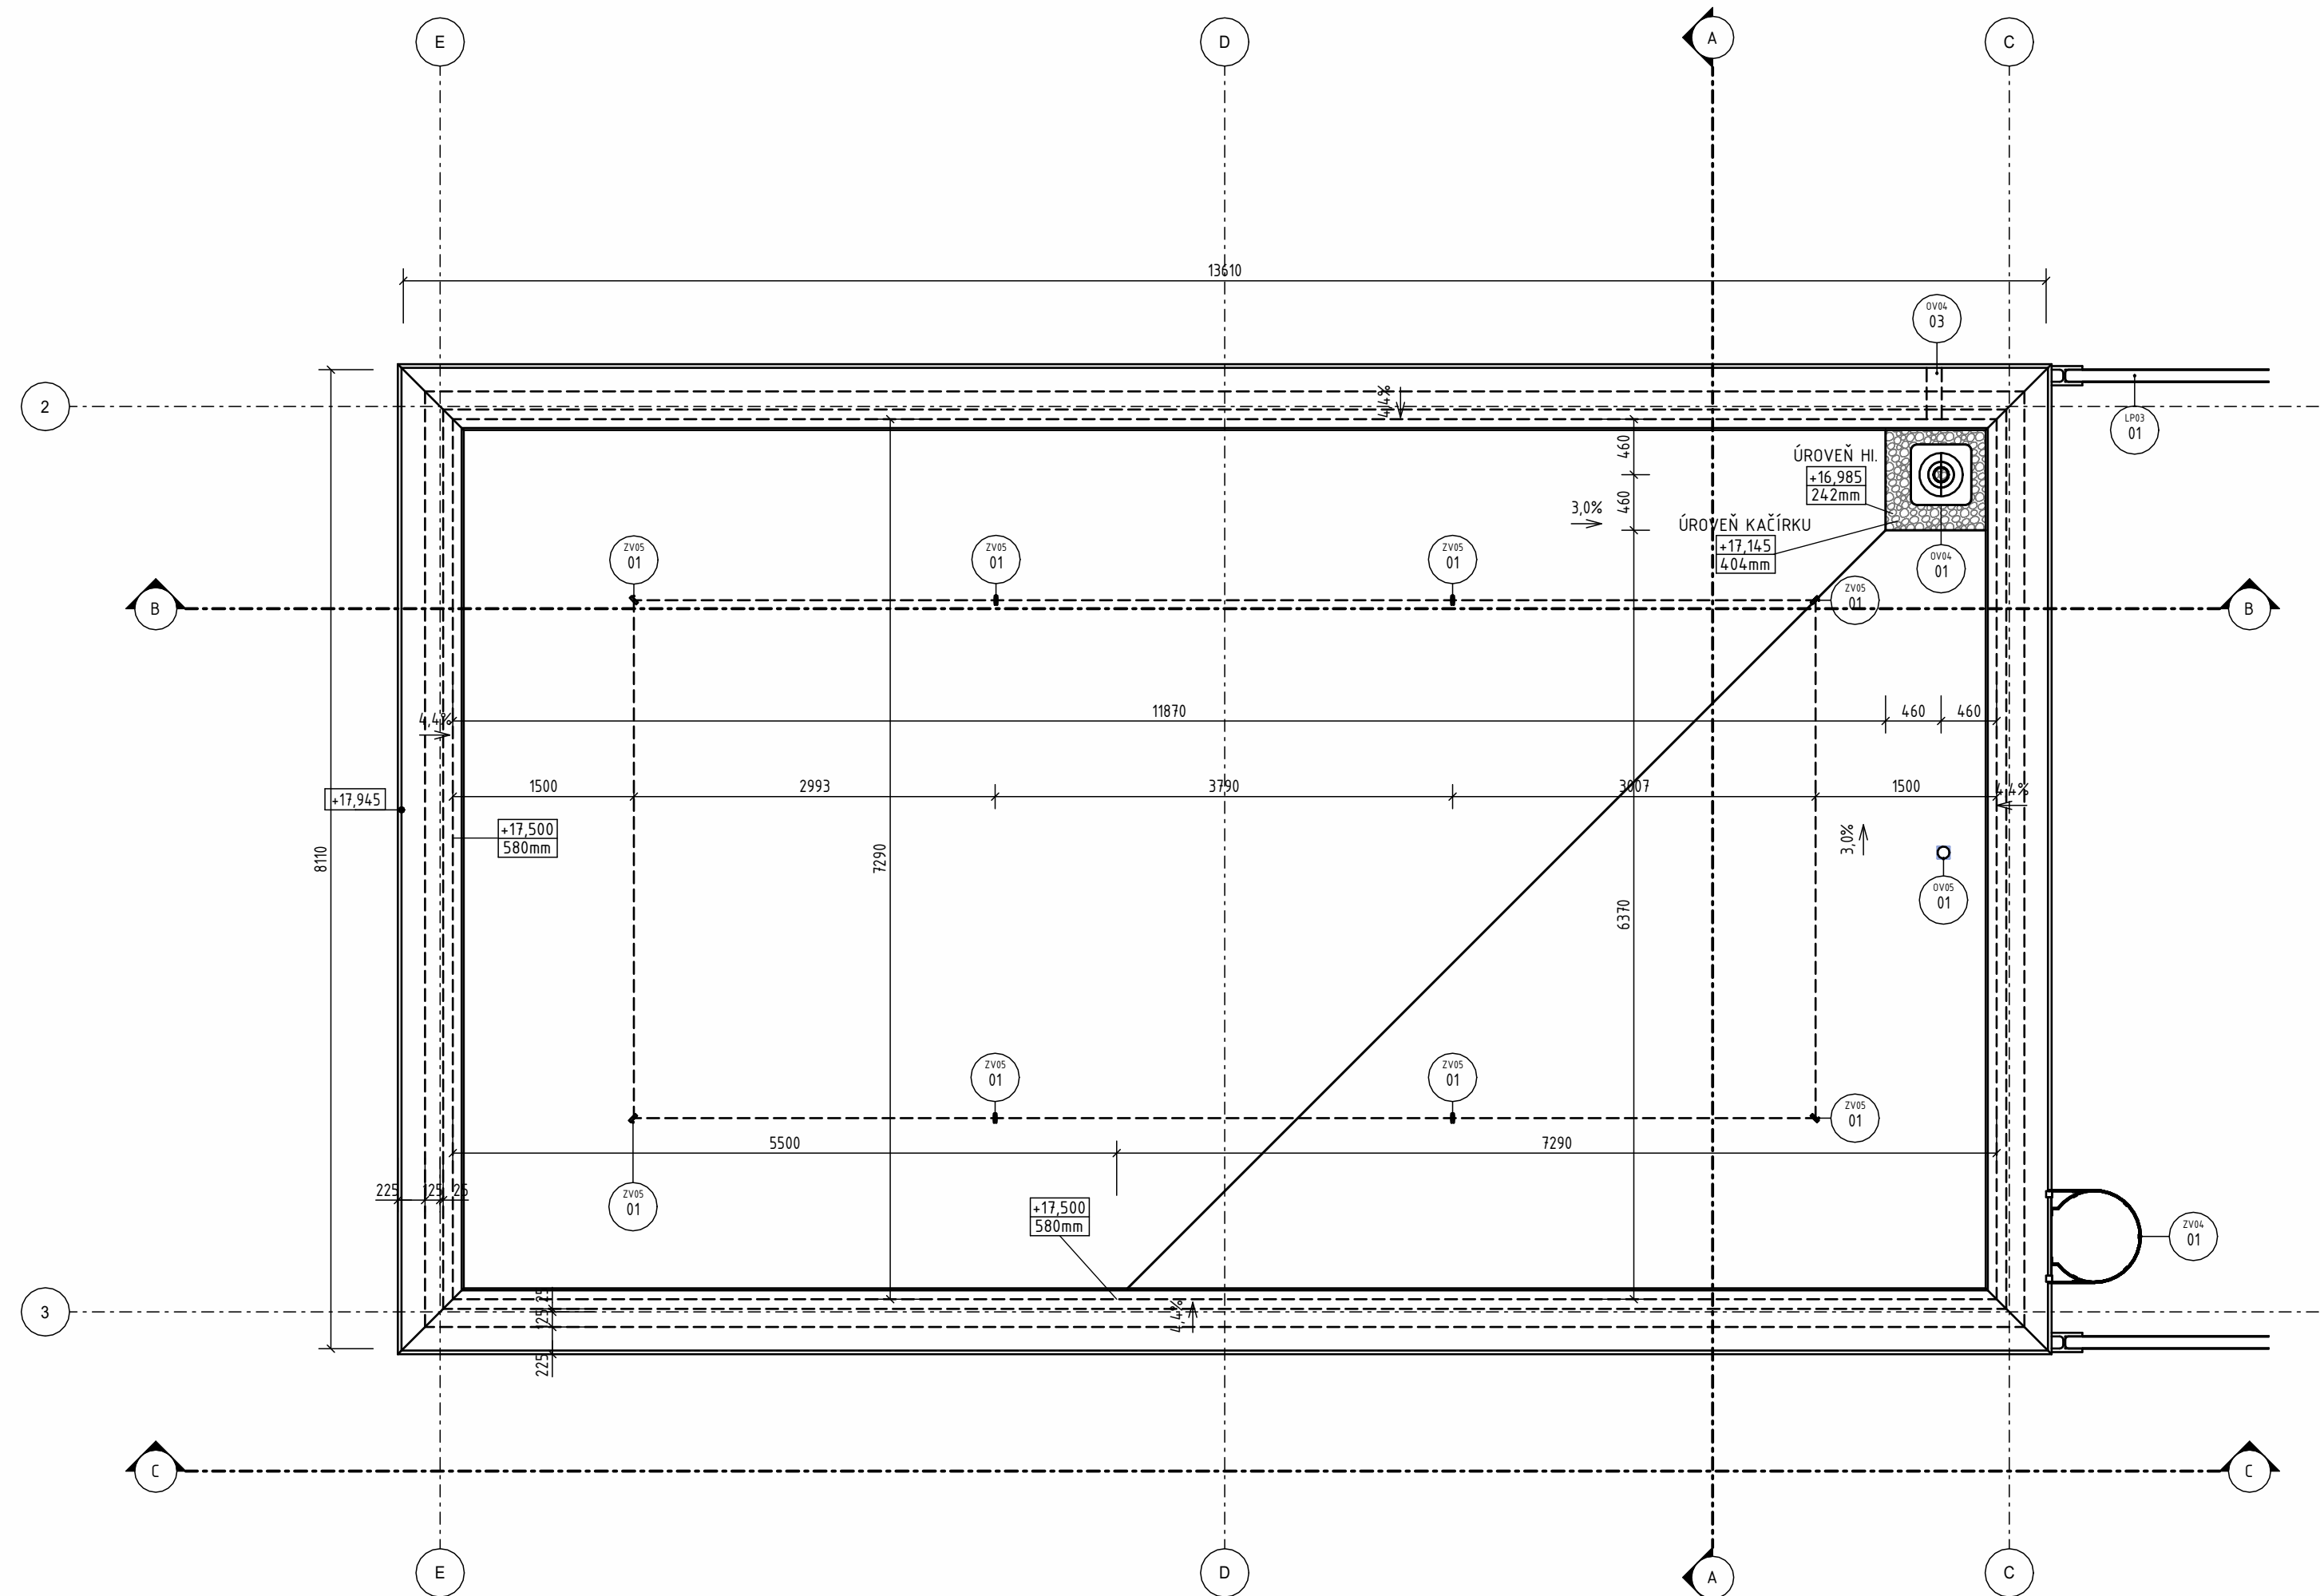

REZ C - POZDÍŽNY REZ STREŠNÝM PLÁŠŤOM

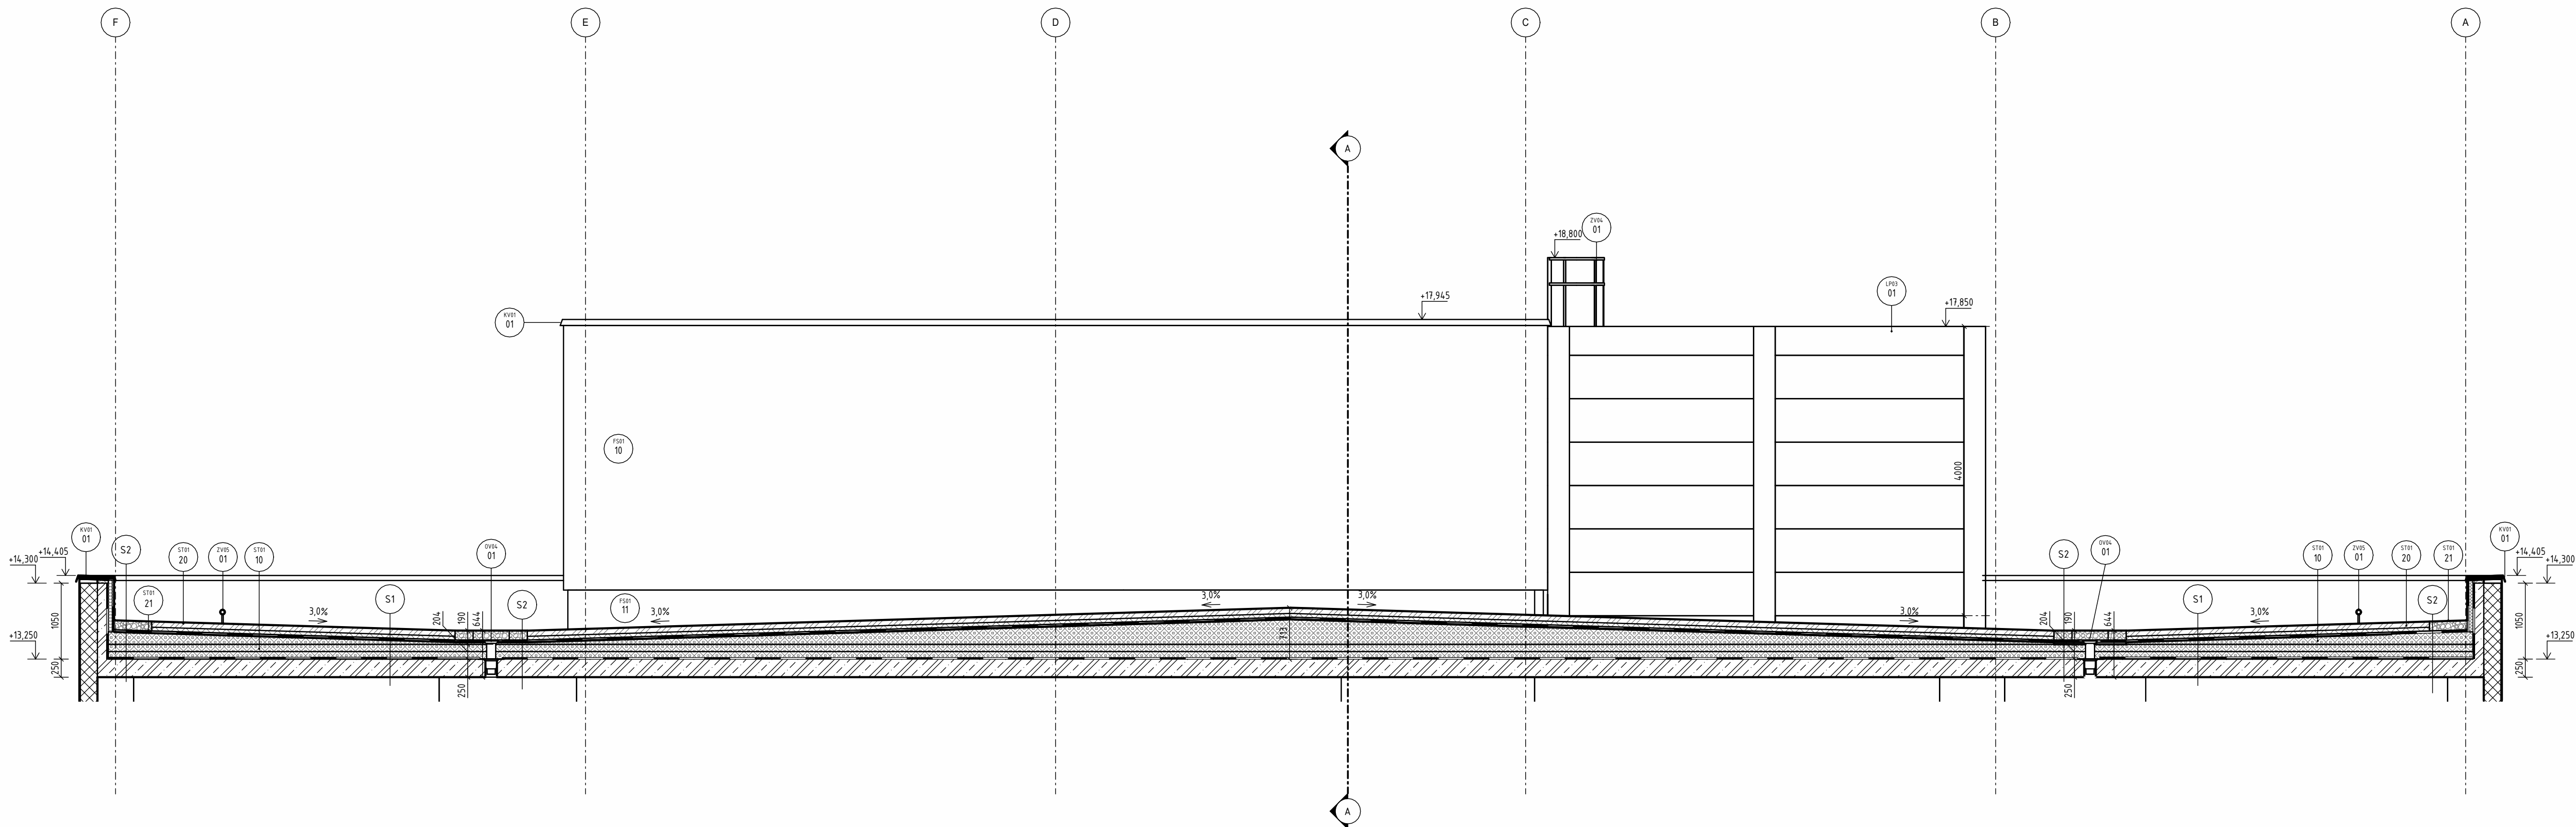

LEGENDA MIESTNOSTÍ

Číslo	Název	Príslúchajúci prístroj	Plocha (m ²)	Svetlo (výkon)	Ponorenie	
					Podlažia	Strop/Podlažia
4.01	Technická miestnosť	Technické priestory	21,8	350	P012.53 - Pangumipho	Bez úpravy
4.02	Elektronizovaná	Technické priestory	16,9	350	P012.53 - Pangumipho	Bez úpravy
4.03	Obchod	Technické priestory	19,11	350	P012.53 - Pangumipho	Bez úpravy
4.04	Elektronizovaná FVE	Technické priestory	4,17	350	P012.53 - Pangumipho	Bez úpravy
50,86						

LEGENDA MATERIÁLOV

	ŽELEZOBETÓN
	PREFABRIKOVANÝ ŽELEZOBETÓN - SOVHOŠKOSÉ RAMENÁ
	PISOLANÝ BETÓN
	SADROKARTÓN
	MURIVO MENŠIÉ
	SADROKARTÓN
	LAKNÝ OBYVOVÝ POKLÁD
	IZOLÁCIA MINERÁLNÁ
	IZOLÁCIA EPS
	IZOLÁCIA XPS
	BETÓNOVÁ DLAŽBA - EXTERIÉR
	KÁČIKEX
	NÁŠYP
	ZEMNIA
	HYDROIZOLÁCIA

LEGENDA ZNAČENIA

FOTOVOLTAICKÝ PANEĽ

POPIŠKA PRÍKOV - SNÍM KÓD

0V D001 - TREDA STAVEBNÉHO PRÍKOV (TSP)
01 D001 - POSTREDA STAVEBNÉHO PRÍKOV (PSP)
00 D000 - UŽÍVATEĽSKÉ OZNAČENIE TYPU (UOT)
00 D001 - IDENTIFIKÁTOR INŠTANČIE (INST)

LEGENDA PRVKOV

[illegible]

POZNÁMKA

[illegible]

K0.000 + 1991 n.m. B.p.v., ÚRADNÝ SYSTÉM JTSK					
PŘEDMET	DIPLOMA PRÁCA				
VYTVÁPČOVACÍ VEDÍC PRÁCE	ING. SAMUEL AUGUSTIN PROF. ING. MILAN OSTRÝ, Ph.D.				
STAVEBNÍ MÍSTO STAVBY	KARL KRODIL INTERVATVA 2, KAŤENANY 821 BRNO, č. PARCELE / 965/1 K.Ú. BRNO-TŘITIA				
NÁZEV STAVBY	OFFICE CENTRUM BRNO				
STAVEBNÝ OBJEKT	S.O.01 POLYPUNKTNYJ OBJEKT				
OBSAH	D.1.1 ARCHITEKTONICO-STAVEBNÉ ŘEŠENÍ				
PÓDRYSY STRUKCHURY					
				FORMAT	A0
				DÁTUM	01/2025
				STUPEŇ PD	I
				MĚŘITVO	X VYKRESU
				1 : 50	B.1104