


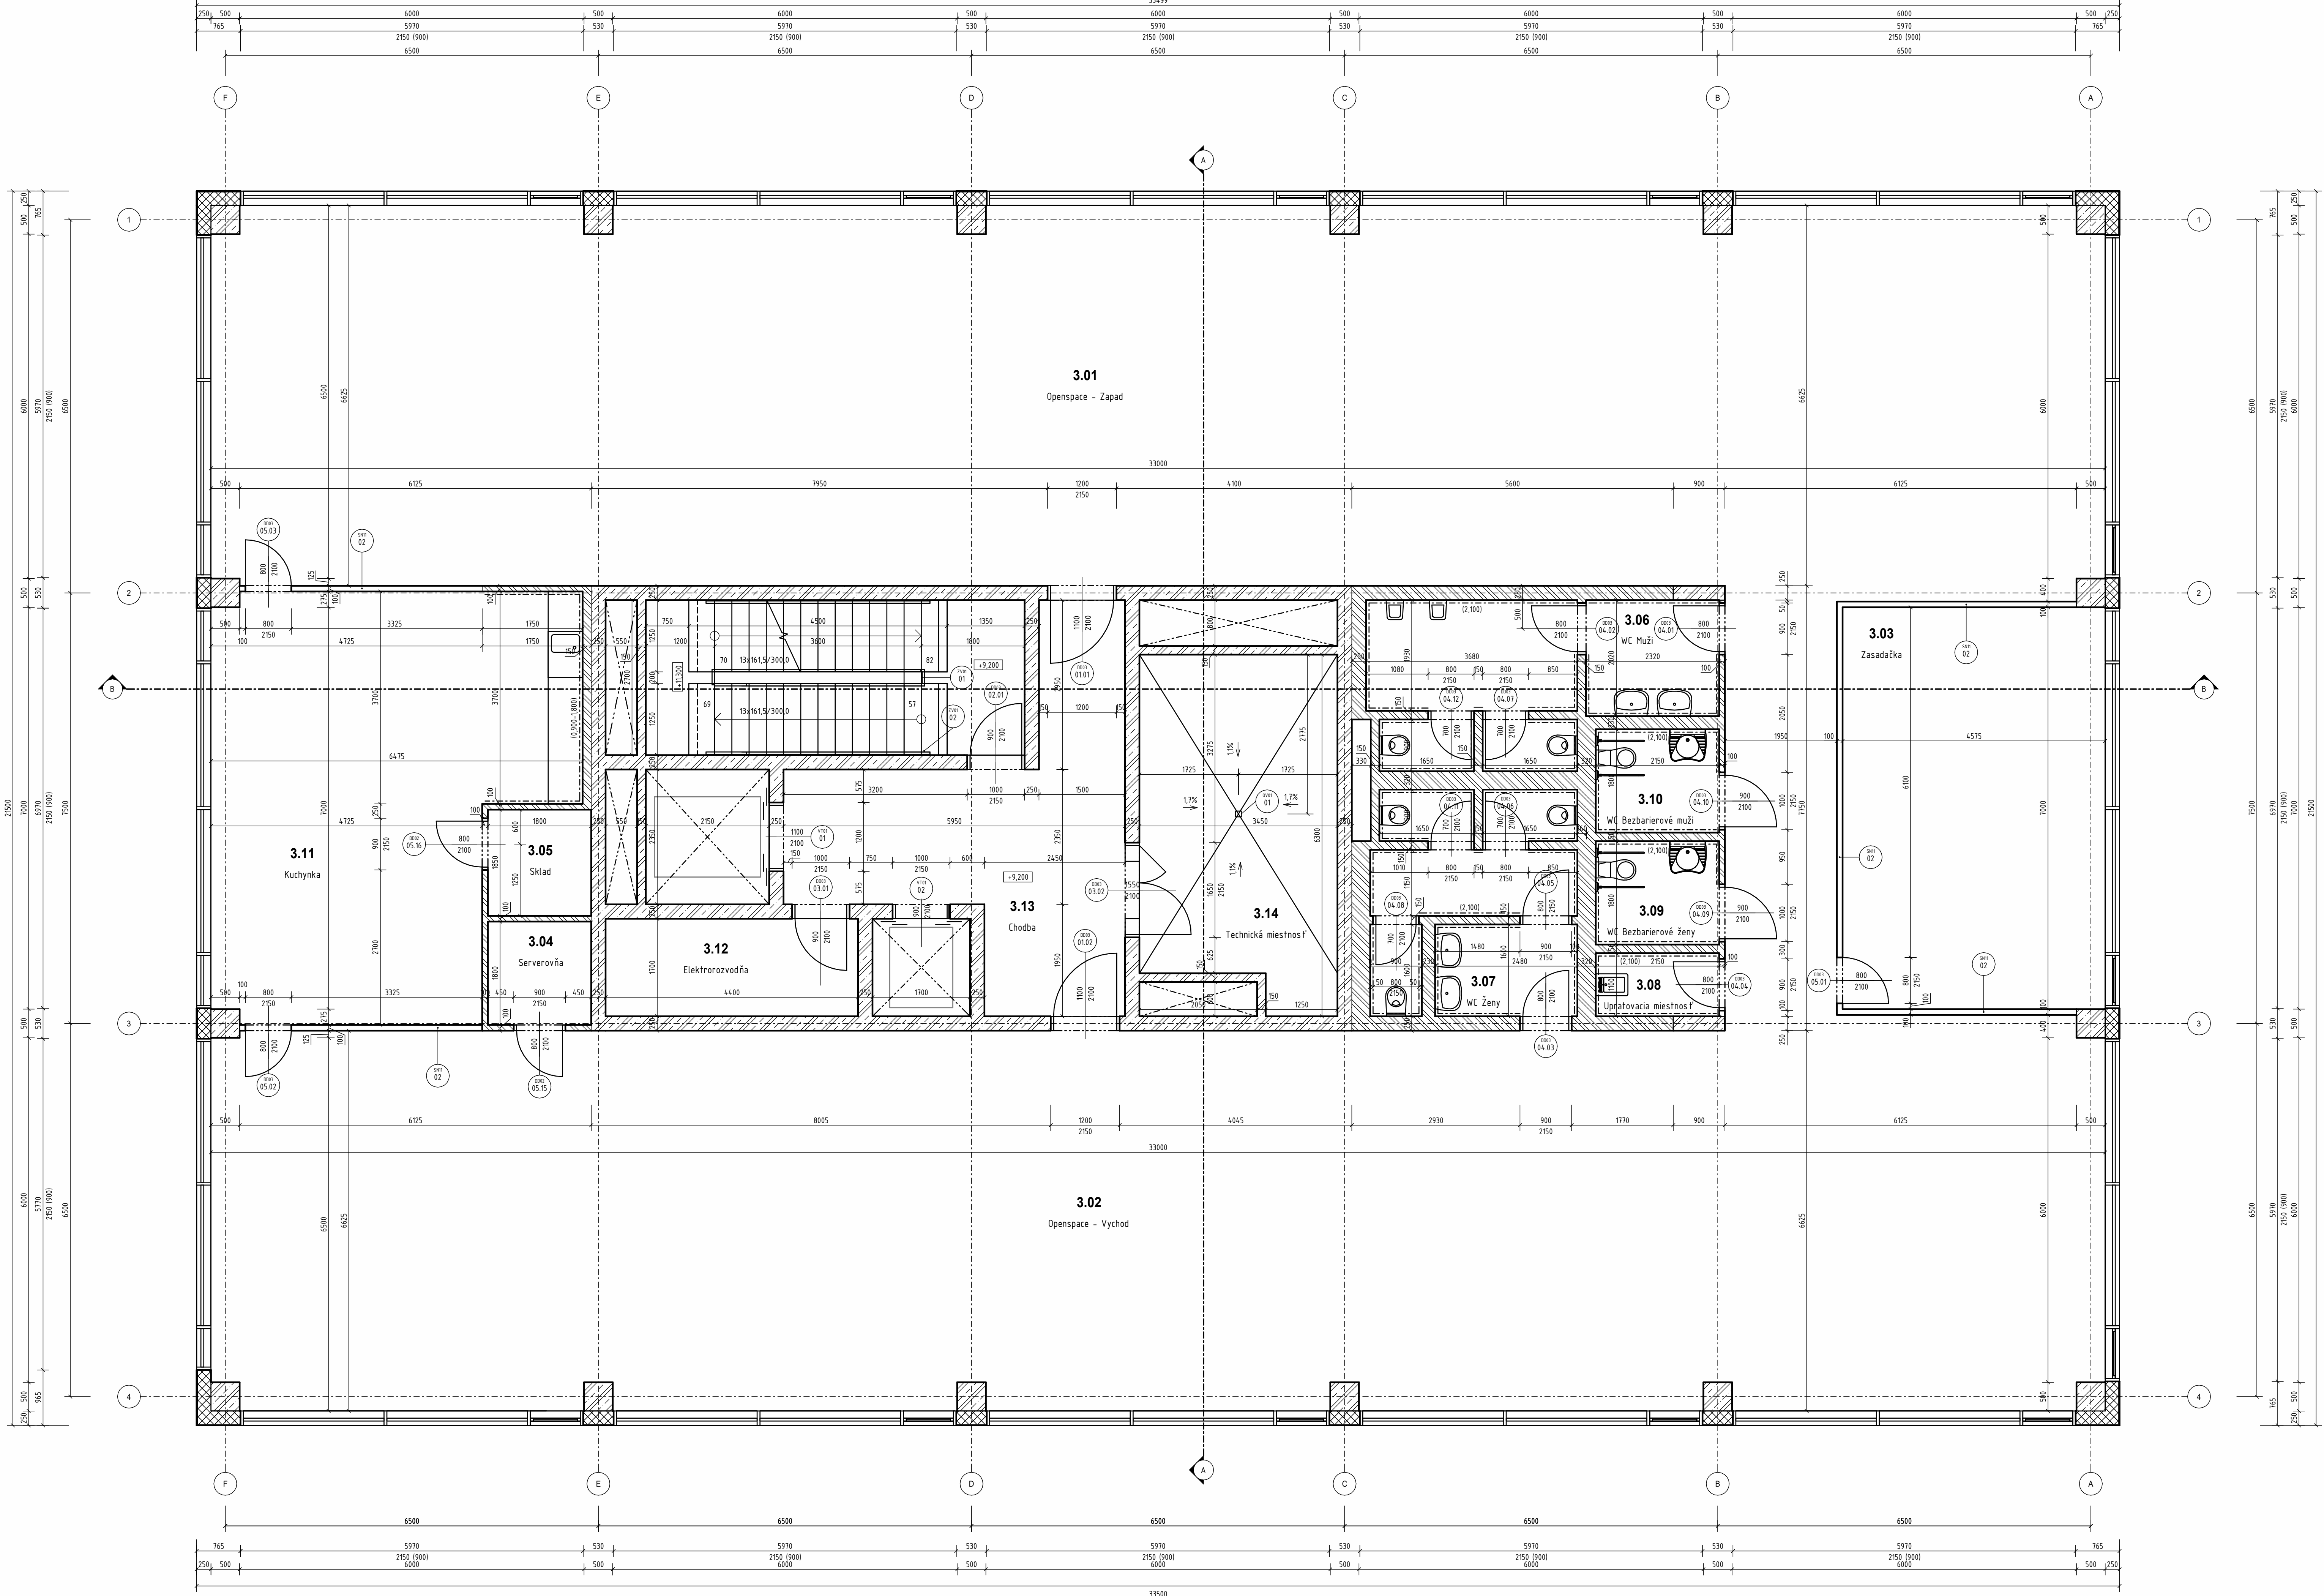

LEGENDA MIESTNOSTÍ

Číslo	Názov	Príslušnosť priestoru	Plocha [m ²]	Svetlá výška [mm]	Podlaha	Povrchy	Steny	Styl miestnosti
3.01	Openspace - Západ	Nájomný priestor	230,95	3050	PD03.30 - Slučkový zářazový koberec	PH01.10 - Kazeľový SDK podlah - štandard	Náher	Openspace
3.02	Openspace - Východ	Nájomný priestor	230,95	3050	PD03.30 - Slučkový zářazový koberec	PH01.10 - Kazeľový SDK podlah - štandard	Náher	Openspace
3.03	Zasadačka	Nájomný priestor	32,90	3050	PD03.31 - Drevená podlaha	PH01.10 - Kazeľový SDK podlah - štandard	Bez úpravy	Zasadačia miestnosť
3.04	Serverovňa	Nájomný priestor	3,24	2600	PD03.60 - Slučkový zářazový koberec	PH01.10 - Kazeľový SDK podlah - štandard	Náher	Sklady, serverovne - NJ
3.05	Sklad	Nájomný priestor	3,33	2600	PD03.60 - Slučkový zářazový koberec	PH01.10 - Kazeľový SDK podlah - štandard	Náher	Sklady, serverovne - NJ
3.06	WC Muži	Nájomný priestor	15,13	2600	PD02.30 - Štvorcová keramická dlažba	PH01.20 - Kazeľový SDK podlah - do vlnka	Keramický obklad, náher	Hygienické zázemie 2-3NP
3.07	WC Ženy	Nájomný priestor	14,10	2600	PD02.30 - Štvorcová keramická dlažba	PH01.20 - Kazeľový SDK podlah - do vlnka	Keramický obklad, náher	Hygienické zázemie 2-3NP
3.08	Upratovacia miestnosť	Nájomný priestor	2,37	2600	PD02.30 - Štvorcová keramická dlažba	PH01.20 - Kazeľový SDK podlah - do vlnka	Keramický obklad, náher	Hygienické zázemie 2-3NP
3.09	WC Bezbarierové ženy	Nájomný priestor	3,87	2600	PD02.30 - Štvorcová keramická dlažba	PH01.20 - Kazeľový SDK podlah - do vlnka	Keramický obklad, náher	Hygienické zázemie 2-3NP
3.10	WC Bezbarierové muži	Nájomný priestor	3,87	2600	PD02.30 - Štvorcová keramická dlažba	PH01.20 - Kazeľový SDK podlah - do vlnka	Keramický obklad, náher	Hygienické zázemie 2-3NP
3.11	Kuchynka	Nájomný priestor	42,75	3050	PD03.70 - Slučkový zářazový koberec	PH01.10 - Kazeľový SDK podlah - štandard	Keramický obklad, náher	Kuchynka - NJ
3.12	Elektronrozvodňa	Technické priestory	7,48	3800	PD02.53 - Antistatický vyvln	PH01.10 - Kazeľový SDK podlah - štandard	Sokol - Antistatický vyvln 100 mm	Elektronrozvodňa 2-3NP
3.13	Chodba	Technické priestory	23,19	3050	PD02.43 - Štvorcová keramická dlažba	PH01.10 - Kazeľový SDK podlah - štandard	Náher	Spoločné priestory - hlavné 2-LNP
3.14	Technická miestnosť	Technické priestory	20,09	3800	PD02.52 - Poropriepustný náterový systém	Bez úpravy	Bez úpravy	Technické priestory 2-3NP

LEGENDA MATERIÁLOV

- ŽELEZOBETÓN
- PREFABRIKOVANÝ ŽELEZOBETÓN - SCHODISKOVÉ RAMENA
- PODKLADNÝ BETÓN
- SADROKARTÓN
- MURIVO NENOSNÉ
- SADROKARTÓN
- LAHKÝ OBVOVÝVÝ PLÁŠT
- IZOLÁCIA MINERÁLNA
- IZOLÁCIA EPS
- IZOLÁCIA XPS
- BETÓNOVÁ DLAŽBA - EXTERIÉR
- KAČÍREK
- NÁSYP
- ZEMINA
- HYDROIZOLÁCIA

LEGENDA ZNAČENIA

- POPISKA PRVKOV - SNH KÓD
- OV (XX) - TREDIA STAVENÉHO PRVKU (TSP)
- 01 (XX) - PODTREDIA STAVENÉHO PRVKU (PSP)
- 00 (XX) - UŽÍVATEĽSKÉ OZNAČENIE TYPU (UOT)
- 00 (XX) - IDENTIFIKÁTOR INŠTANCIE (INST)

LEGENDA PRVKOV

TSP/PSP/UOT	Popis prvku
SN11 02	Sklenená priečka, bezrámová, dvojité zasklenie, ref. výrobok LKOS - MIRA II
ZV01 01	Schodiskové zberadlie výšky 1000 mm, osadené stĺpkami na schodiskovom ramene
ZV01 02	Schodiskové zberadlie výšky 1000 mm, osadené na žb stene
OV01 01	Výpusť podlahy, DN10, krytá pochádzajú z mriežkou

POZNÁMKY

- Kótované v koordinátnych rozmeroch
- Súčasťou výkresovej dokumentácie je technická správa, v prípade rozporu TS a výkresový PD, konzultovať s projektantom
- Pri vyhotovovaní stavby je nutné postupovať podľa platných ČSN a odsúhlasených technologických postupov
- Pri stavebných prácach musia byť dodržané platné predpisy týkajúce sa zásad a bezpečnosti ochrany zdravia pri práci
- Typ navrhnutého LOP Schuco PWS 50.53, U₁₀ = 0,04 W/m²K, otváracie okenné výplne sú zhodné vo všetkých prípadoch - viz. prílohy, pri osadzovaní panelov postupovať podľa pokynov výrobcu, typové detaily a podrobný teplotechnický výpočet viz. prílohy
- V miestnostiach s rôznymi skladbami podlahy budú osadené prechodové lišty
- Charakteristický jednotlivých konštrukcií a prvkov v d. výpis sklaieb
- Pri keramickom murive osadenie príslušného typu prekrytu podľa výberu konkrétneho výrobku
- V priestore odpadového hospodárstva na dverách alebo LOP budú osadené prefabrikované mriežky, súčasťou podrobného návrhu profosie VZT
- Priečky a nenosné steny budú ukončené spôsobom, že medzi hornou hranou priečky a stropom ostane medzera hr. 10-15 mm, ktorá bude vyplnená montážnou penou, alebo do nej bude vliatelná minerálna plsť, podľa pokynov dodávateľa
- Skladby sadrokartónových priečok skenerizované v ďalšom stupni PD, s ohľadom na výsledky posúdenia stavebnej fyziky, osadené podľa typu priestorová, nutné zachovať minimálny rozmer miestnosti, ref. výrobky Knauf WTS a Knauf WTS
- Prefabrikované schodiskové rameno opatříť sferkou hrúbky a typu produktu užíteľu na podestiat
- Schodiskové rameno osadí na prýžové podložky
- Nástupné a výstupné stupne schodiska kontrastne odlišť
- Výstup schodiskových podestiat urobiť do systému ochrany proti kroľákovému zvuku, ref. výrobky Schick Tronoste
- Všetky prestupy požiarne deliacimi konštrukciami musia byť riadne utužené podľa ustanovenia PR05
- Plávajúce podlahy budú dilatované pod obvode miestnosti
- Prestupy v základovej doske musia byť riadne utužené proti vode a radónu
- Materiálové charakteristiky betónu a zele budú doplnené na základe podrobného statickej analýzy autorizovanou osobou
- Zariadenie pomocou kódov SNH je v tomto projekte stanovené podľa tabuľky hierarchie v prílohe

±0,000 = 199,1 m n.m., B.p.v., SÚRADNICOVÝ SYSTÉM JTSK

PREDMET	DIPLLOMOVÁ PRÁCA			FORMÁT	1150x594
VYPRACOVAL	ING. SAMUEL AUGUSTÍN				
VEDÚCI PRÁCE	PROF. ING. MILAN OSTRÝ Ph.D.				
STAVEBNÍK	KAROL OLDŘICH, INTERNÁTOVÁ 2, KAMEŇANY 821				
MIESTO STAVBY	BRNO, č. PARCELY 966/1, K.Ú. BRNO-TRNITÁ		STUPEŇ PD	Č. VÝKRESU	
NÁZOV STAVBY	OFFICE CENTRUM BRNO				
STAVEBNÝ OBJEKT	SO.01 POLYFUNKČNÝ OBJEKT				
ČASŤ	0.11 ARCHITEKTONICKO-STAVEBNÉ RIŠENIE		MERÍTKO	1 : 50	D.11.03
OBSAH:	PÓDORYS 3NP				